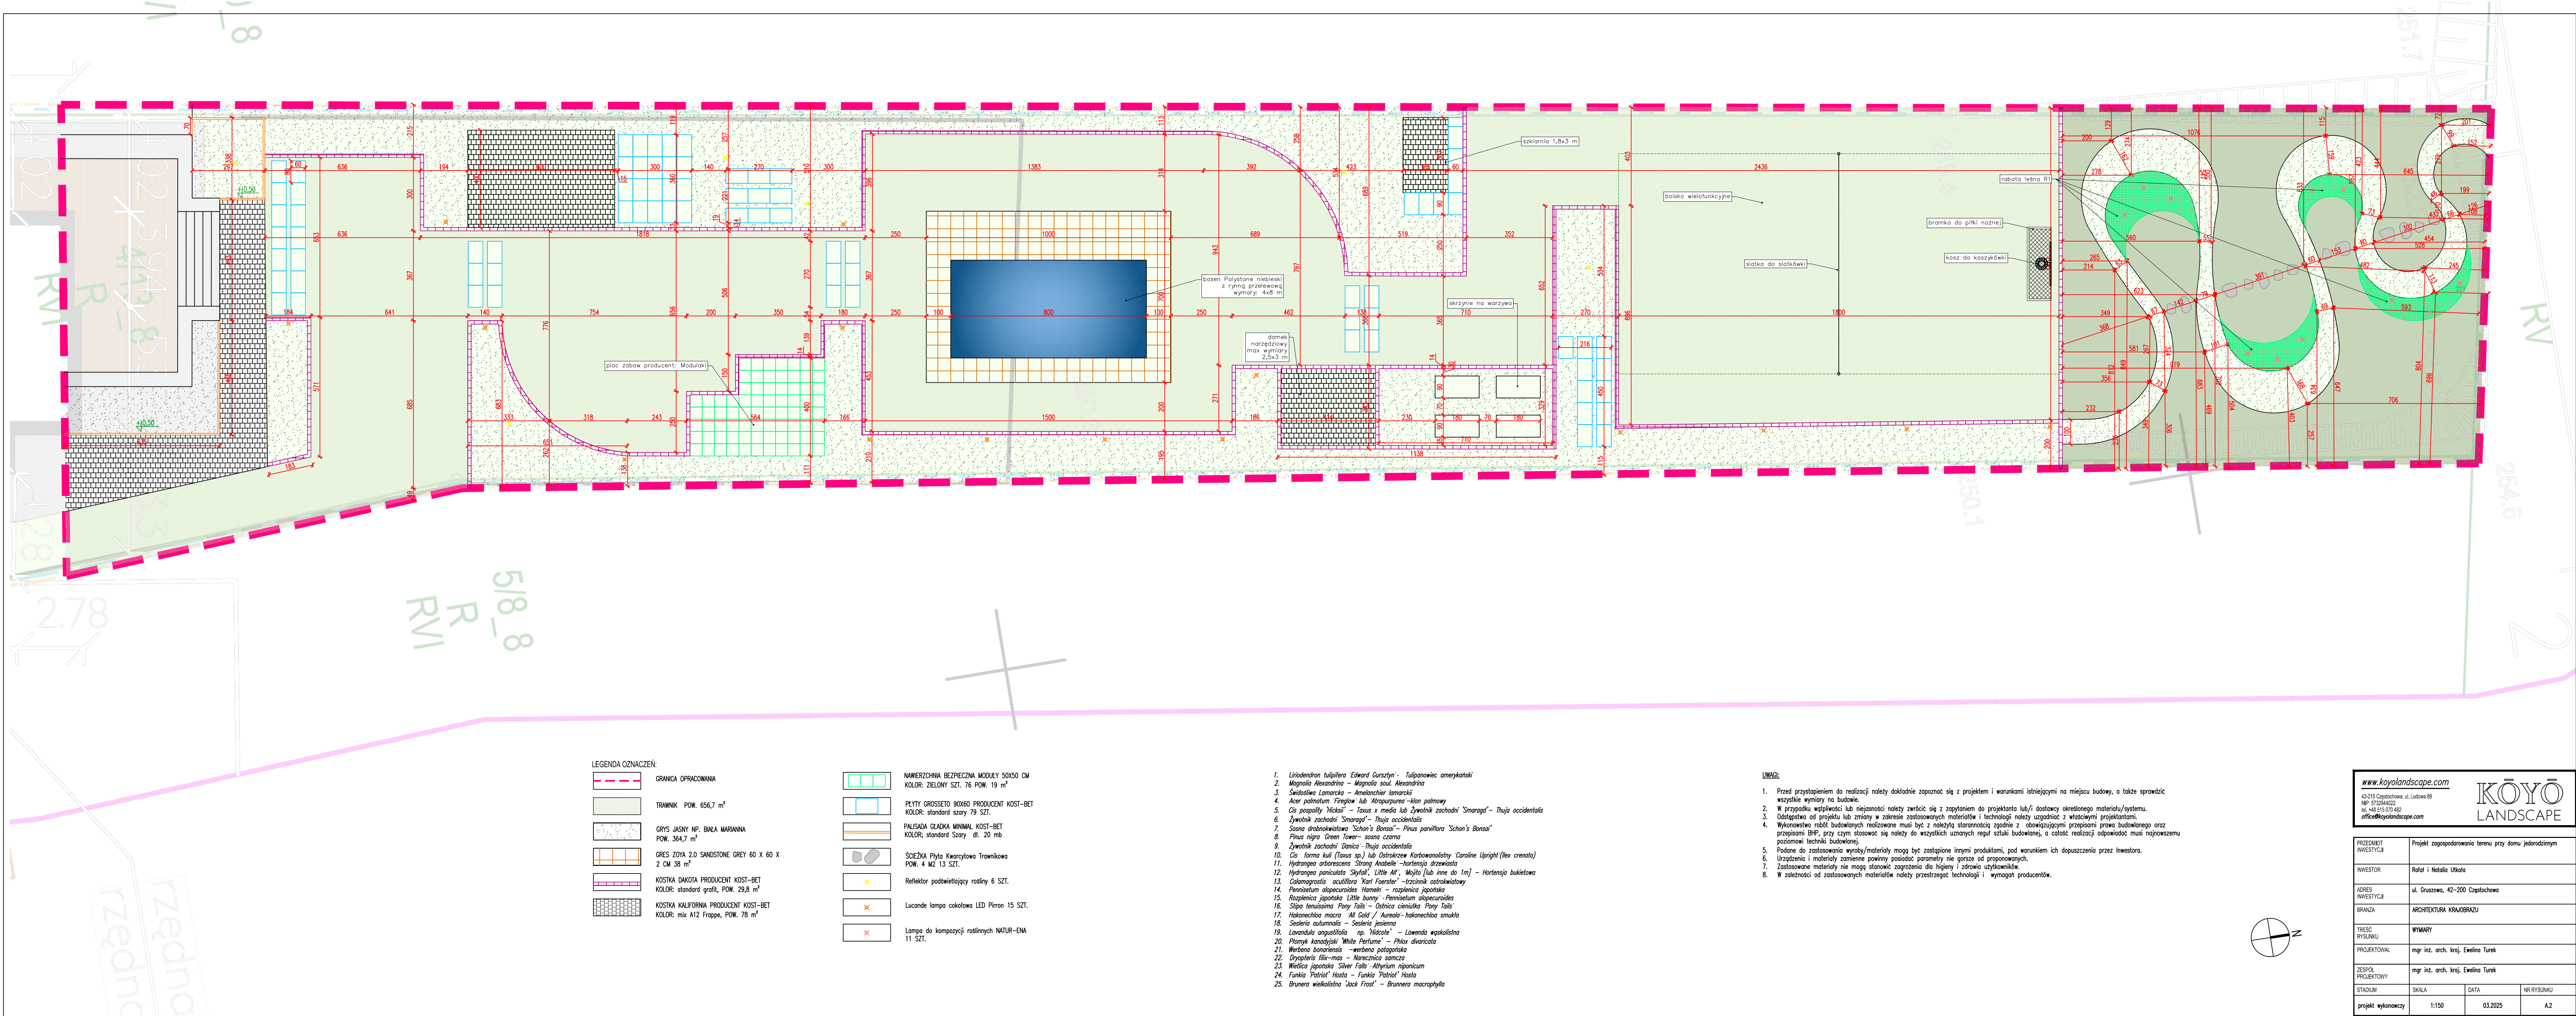


www.koyolandscape.com 62-535 Częstochowa, ul. Ludowa 89 NIP: 572264022 tel. +48 515 070 432 office@koyolandscape.com			
KŌYŌ LANDSCAPE			
PRZEDMIOT INWESTYCJI	Projekt zagospodarowania terenu przy domu jednorodzinnym		
INWESTOR	Rafał i Natalia Ułkoła		
ADRES INWESTYCJI	ul. Gruzowa, 42-200 Częstochowa		
BRANŻA	ARCHITECTURA KRAJOBRZĄDU		
TREŚĆ RYSUNKU	WYMIARY		
PROJEKTOWAŁ	mgr inż. arch. kraj. Ewelina Turak		
ZESPÓŁ PROJEKTOWY	mgr inż. arch. kraj. Ewelina Turak		
STADIUM	SKALA	DATA	NR RYSUNKU
projekt wykonawczy	1:150	03.2025	A2