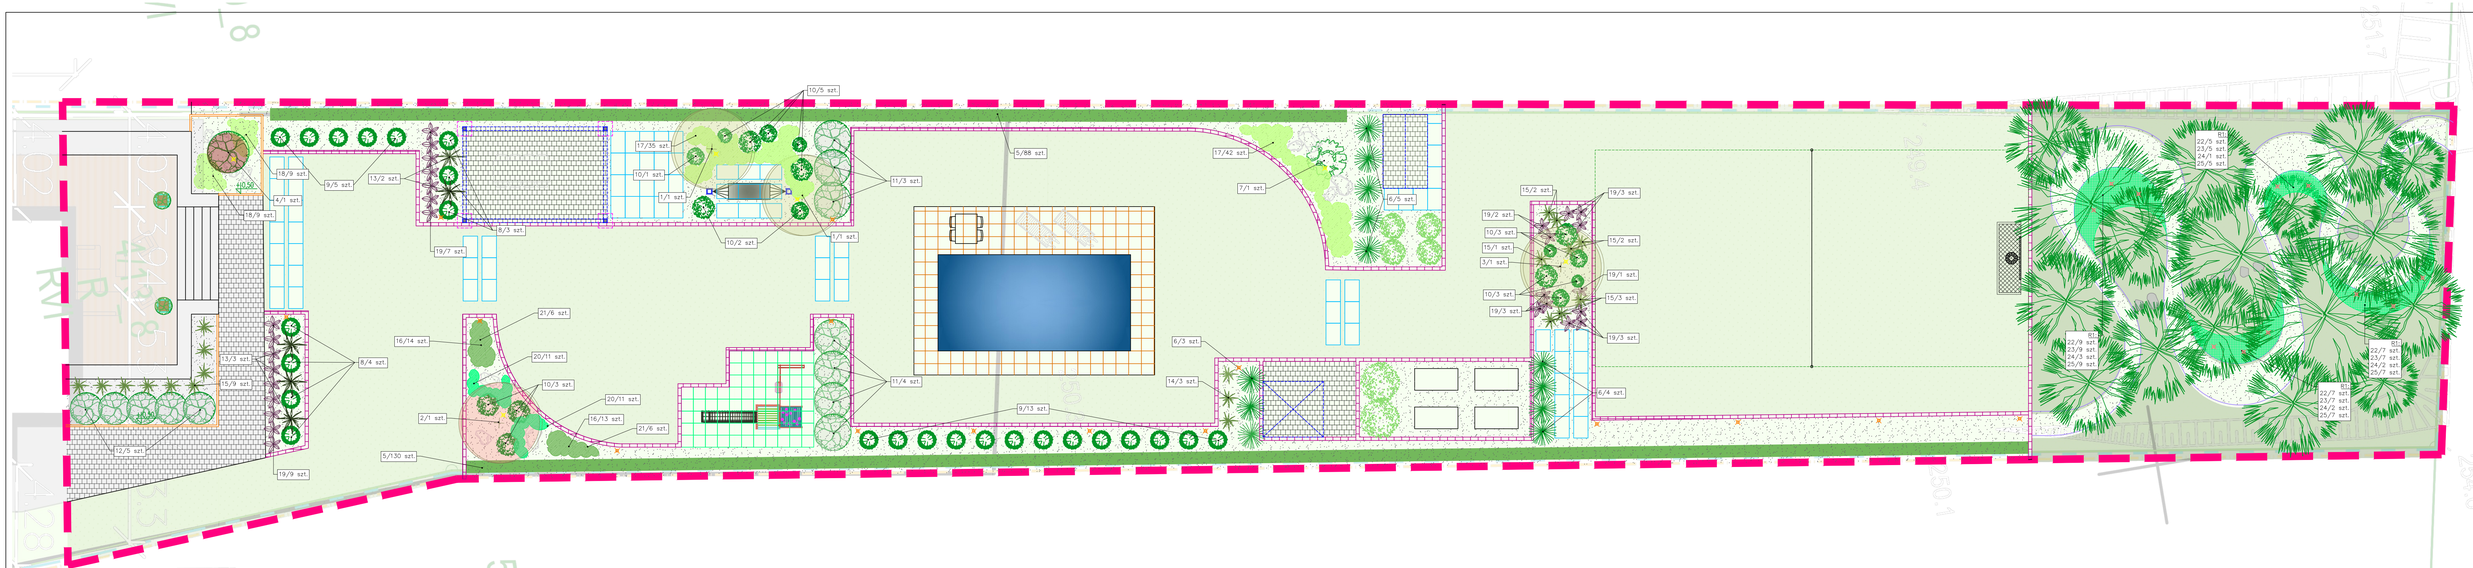


LEGENDA OZNACZEŃ:

- GRANICA OPRACOWANIA
- TRAWNIK POW. 656,7 m²
- GRYS JASNY NP. BARA MARIANNA POW. 364,7 m²
- GRES ZOYA 2.0 SANDSTONE GREY 60 X 60 X 2 CM 38 m²
- KOSTKA DAKOTA PRODUCENT KOST-BET KOLOR: standard grafit, POW. 29,8 m²
- KOSTKA KALIFORNIA PRODUCENT KOST-BET KOLOR: mix A12 Frappe, POW. 78 m²
- OBRZEŻE EKO-BORD DL. 117 mb
- NAWIERZCHNIA BEZPIECZNA MODUŁY 50X50 CM KOLOR: ZIELONY SZT. 76 POW. 19 m²
- PŁYTY GROSSETO 90X60 PRODUCENT KOST-BET KOLOR: standard szary 79 SZT.
- PALISADA CLADRA MINIMAL KOST-BET KOLOR: standard Szary dł. 20 mb
- ŚCIEŻKA Płyta Kwarcytowa Trawnikowa POW. 4 M2 13 SZT.
- Reflektor podświetlający rośliny 6 SZT.
- Lucande lampa ogrodowa LED Pirron 15 SZT.
- Lampa do kompozycji roślinnych NATUR-ENA 11 SZT.

1. *Liriodendron tulipifera Edward Gursztyn – Tulipanowiec amerykański*
2. *Magnolia Alexandrina – Magnolia soul. Alexandrina*
3. *Świdośliwa Lamarcka – Amelanchier lamarckii*
4. *Acer palmatum 'Fireglow' lub 'Atropurpurea' –klon palmowy*
5. *Cis pospolity 'Hicksii' – Taxus x media lub Żywotnik zachodni 'Smaragd' – Thuja occidentalis*
6. *Żywotnik zachodni 'Smaragd' – Thuja occidentalis*
7. *Sosna drobnokwiatowa 'Schon's Bonsai'– Pinus parviflora 'Schon's Bonsai'*
8. *Pinus nigra 'Green Tower'– sosna czarna*
9. *Żywotnik zachodni 'Danica '-Thuja occidentalis*
10. *Cis forma kuli (Taxus sp.) lub Ostrokrzew Kerbowonalistny 'Caroline Upright'(Ilex crenata)*
11. *Hydrangea arborescens 'Strong Anabelle' –hortensja drzewiasta*
12. *Hydrangea paniculata 'Skyfall', 'Little Ali', 'Mojito'(lub inne do 1m) – Hortensja bukietowa*
13. *Calamagrostis acutiflora 'Karl Foerster' –trzcinnik ostrokwiatowy*
14. *Pennisetum alopecuroides 'Hameln' – rozplenica japońska*
15. *Rozplenica japońska 'Little Bunny - Pennisetum alopecuroides*
16. *Stipa tenuissima 'Pony Tails' – Ostnica cienuśka 'Pony Tails'*
17. *Hakonechloa macra 'All Gold' / 'Aureola'- hakonechloa smukła*
18. *Sesleria autumnalis – Sesleria jesienna*
19. *Lavandula angustifolia ep. 'Nidzate' – Lawenda wąskolistna*
20. *Płomyk kanadyjski 'White Perfume' – Phlox divaricata*
21. *Werbena bonariensis – werbena patagońska*
22. *Dryopteris filix-mas – Narecznica samcza*
23. *Wietlica japońska 'Silver Falls' -Athyrium nipponicum*
24. *Funkia 'Patriot' Hosta – Funkia 'Patriot' Hosta*
25. *Brunera wielkolistna 'Jack Frost' – Brunnera macrophylla*

UWAGI:

1. Przed przystąpieniem do realizacji należy dokładnie zapoznać się z projektem i warunkami istniejącymi na miejscu budowy, a także sprawdzić wszystkie wymiary na budowie.
2. W przypadku wątpliwości lub niejasności należy zwrócić się z zapytaniem do projektanta lub/i dostawcy określonego materiału/systemu.
3. Odstępstwa od projektu lub zmiany w zakresie zastosowanych materiałów i technologii należy uzgadniać z właściwym projektantami.
4. Wykonawcy robót budowlanych realizowane musi być z należytą starannością zgodnie z obowiązującymi przepisami prawa budowlanego oraz przepisami BHP, przy czym stosowac się należy do wszystkich uznanych reguł sztuki budowlanej, a całość realizacji odpowiadać musi najnowszemu poziomowi techniki budowlanej.
5. Podane do zastosowania wyroby/materiały mogą być zastąpione innymi produktami, pod warunkiem ich dopuszczenia przez Inwestora.
6. Urządzenia i materiały zamienne powinny posiadać parametry nie gorsze od proponowanych.
7. Zastosowane materiały nie mogą stanowić zagrożenia dla higieny i zdrowia użytkowników.
8. W zależności od zastosowanych materiałów należy przestrzegać technologii i wymagań producentów.

www.koyolandscape.com
42-215 Częstochowa, ul. Ludowa 89
NIP: 5732944022
tel. +48 515 070 482
office@koyolandscape.com

KOYO LANDSCAPE

PRZEDMIOT INWESTYCJI	Projekt zagospodarowania terenu przy domu jednorodzinnym
INWESTOR	Rafał i Natalia Ulkalla
ADRES INWESTYCJI	ul. Gruszowa, 42-200 Częstochowa
BRANŻA	ARCHITEKTURA KRAJOBRAZU
TREŚĆ RYSUNKU	PROJEKT NASADZEŃ
PROJEKTOWAŁ	mgr inż. arch. kraj. Ewelina Turek
ZESPÓŁ PROJEKTOWY	mgr inż. arch. kraj. Ewelina Turek

STADIUM	SKALA	DATA	NR RYSUNKU
projekt wykonawczy	1:150	03.2025	A.3