


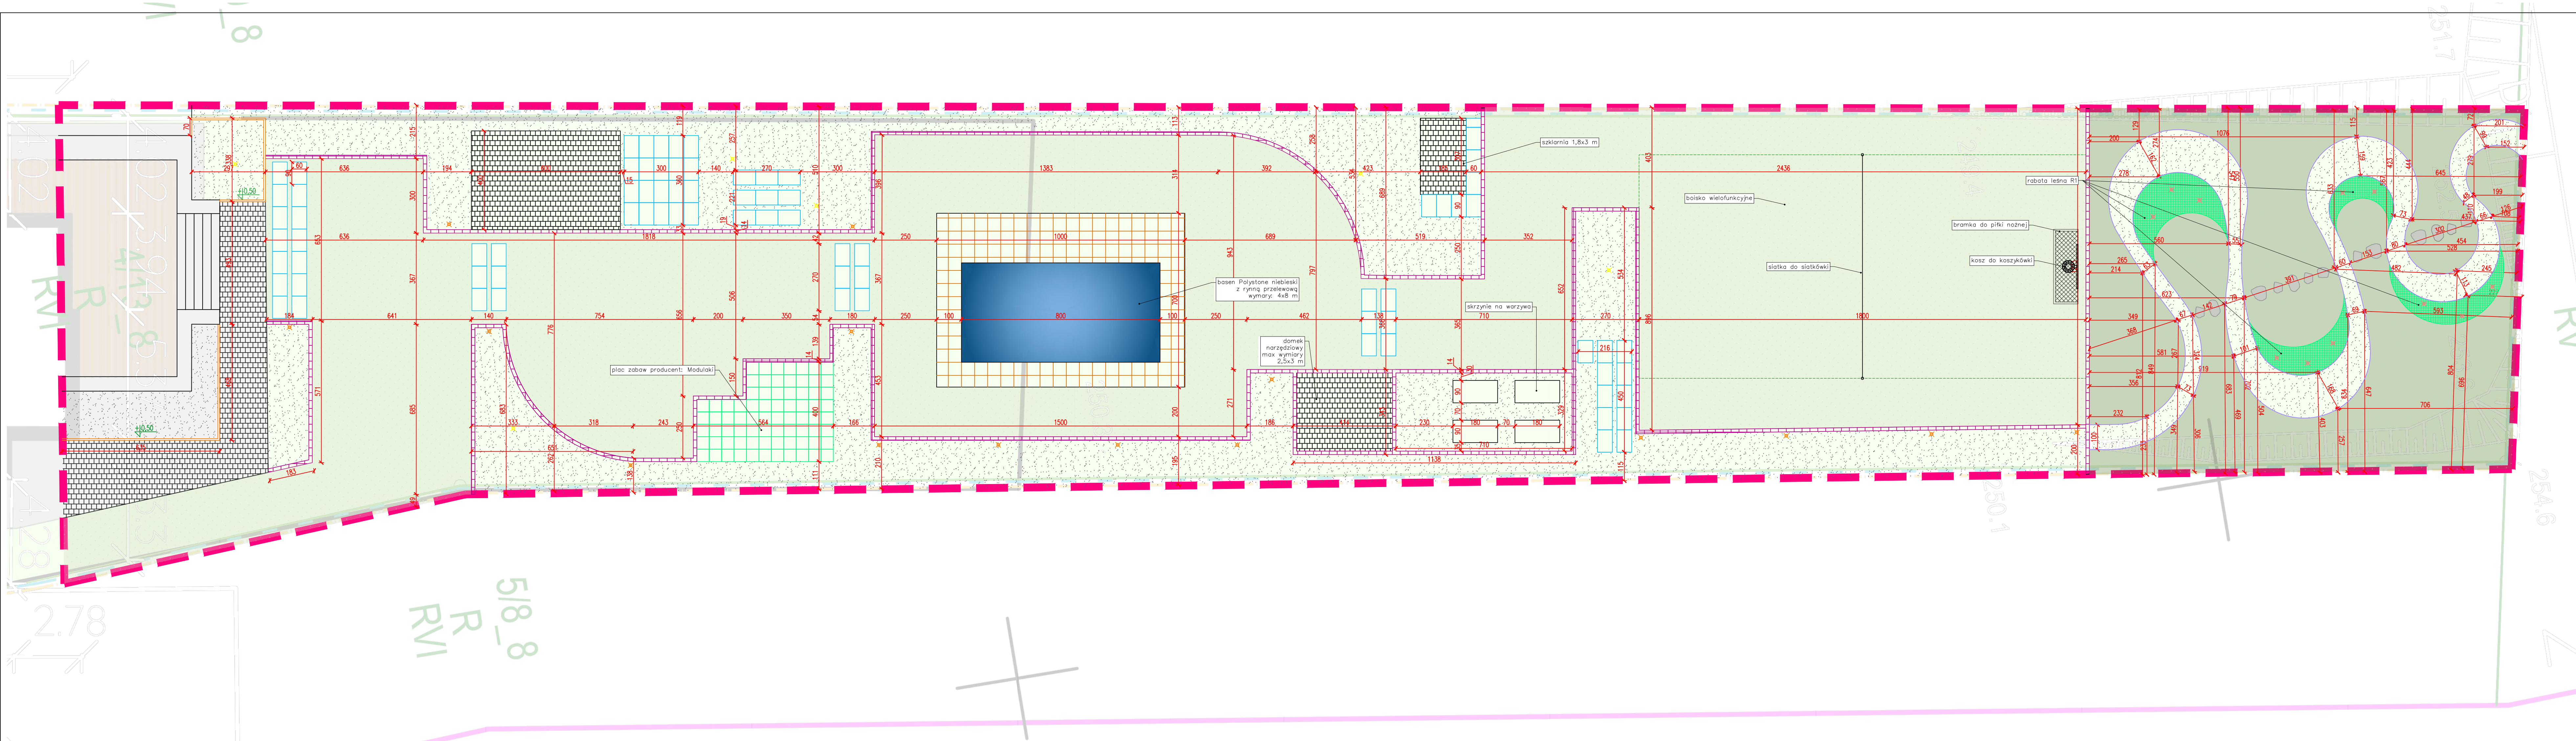

LEGENDA OZNACZEN:

- GRANICA OPRACOWANIA
- TRAWNIK POW. 656,7 m²
- GRYS JASNY NP. BIAŁA MARIANNA POW. 364,7 m²
- GRES ZOYA 2.0 SANDSTONE GREY 60 X 60 X 2 CM 38 m²
- KOSTKA DAKOTA PRODUCENT KOST-BET KOLOR: standard grafit, POW. 29,8 m²
- KOSTKA KALIFORNIA PRODUCENT KOST-BET KOLOR: mix A12 Froppé, POW. 78 m²
- OBREZĘŻE EKO-BORD DL. 117 mb

- NAWIERZCHNIA BEZPIECZNA MODUŁY 50X50 CM KOLOR: ZIELONY SZT. 76 POW. 19 m²
- PLYTY GROSSETO 90X60 PRODUCENT KOST-BET KOLOR: standard szary 79 SZT.
- PAŁISADA GŁADKA MINIMAL KOST-BET KOLOR: standard Szary dl. 20 mb
- ŚCIEŻKA Płyta Kwarcytowa Trawnikowa POW. 4 M2 13 SZT.
- Reflektor podświetlający rośliny 6 SZT.
- Lucone lampa cokolowa LED Pirron 15 SZT.
- Lampa do kompozycji roślinnych NATUR-ENA 11 SZT.

- Liriodendron tulipifera* 'Edward Gursztyn' - Tulipanowiec amerykański
- Magnolia Alexandrina* - Magnolia soul. Alexandrina
- Świdłowa Lamarcka* - Amelanchier lamarckii
- Acer palmatum* 'Fireglow' lub *Atraphaxipurea* - klon palmowy
- Cis pascuifolii* 'Hicksi' - *Taxus media* lub *Żywotnik zachodni* 'Smaragd' - *Thuja occidentalis*
- Żywotnik zachodni* 'Smaragd' - *Thuja occidentalis*
- Sosna drabankowata* 'Schan's Bonsai' - *Pinus parviflora* 'Schan's Bonsai'
- Pinus nigra* 'Green Tower' - sosna czarna
- Żywotnik zachodni* 'Danica' - *Thuja occidentalis*
- Cis forma kuli* (*Taxus sp.*) lub *Ostrykrzew Karbowanołstny* 'Caroline Upright' (*Ilex crenata*)
- Hydrangea arborescens* 'Strong Anabelle' - hortensja drzewiasta
- Hydrangea paniculata* 'Sylfide' 'Little 4H' 'Mojito' (lub inne do 1m) - Hortensja bukitowa
- Osłomagrostis acutiflora* 'Karl Foerster' - trzcinnik ostrzałkowaty
- Pennisetum alopecuroides* 'Hameln' - rozplenica japońska
- Rozplenica japońska 'Little bunny' - *Pennisetum alopecuroides*
- Slipa tenuissima* 'Pony Tails' - Oślnica cienkolutka 'Pony Tails'
- Hakonechloa macra* 'All Gold' / *Aureola* - *hakonechloa smukła*
- Sesleria autumnalis* - *Sesleria jesienna*
- Lavandula angustifolia* np. 'Hidcote' - Lawenda wąskolistna
- Plomyk kanadyjski 'White Perfume' - *Phlox divaricata*
- Verbena bonariensis* - *werbena patagajska*
- Dryopteris filix-mas* - *Narecznica samcza*
- Wiellica japońska 'Silver Falls' - *Allyrium niponicum*
- Funkia 'Patriot' Hosta - Funkia 'Patriot' Hosta
- Brunera wielkolistna* 'Jack Frost' - *Brunnera macrophylla*

UWAGI:

- Przed przystąpieniem do realizacji należy dokładnie zapoznać się z projektem i warunkami istniejącymi na miejscu budowy, a także sprawdzić wszystkie wymiary na budowie.
- W przypadku wątpliwości lub niejasności należy zwrócić się z zapytaniem do projektanta lub/i dostawcy określonego materiału/systemu.
- Odstąpienie od projektu lub zmiany w zakresie zastosowanych materiałów i technologii należy uzgodnić z właściwymi projektantami.
- Wykonawstwo robót budowlanych realizowane musi być z należytą starannością zgodnie z obowiązującymi przepisami prawa budowlanego oraz przepisami BHP, przy czym stosować się należy do wszystkich uznanych reguł sztuki budowlanej, a całość realizacji odpowiadać musi najnowszemu poziomowi techniki budowlanej.
- Podane do zastosowania wyroby/materiały mogą być zastąpione innymi produktami, pod warunkiem ich dopuszczenia przez Inwestora.
- Urządzenia i materiały zamienne powinny posiadać parametry nie gorsze od proponowanych.
- Zastosowane materiały nie mogą stanowić zagrożenia dla higieny i zdrowia użytkowników.
- W zależności od zastosowanych materiałów należy przestrzegać technologii i wymagań producentów.

www.koyolandscape.com 42-215 Częstochowa, ul. Ludowa 88 NIP: 5722844022 tel: +48 515 070 402 office@koyolandscape.com KOYO LANDSCAPE			
PRZEMOT INWESTYCJI	Projekt zagospodarowania terenu przy domu jednorodzinnym		
INWESTOR	Rafał i Natalia Utko		
ADRES INWESTYCJI	ul. Gruszcowa, 42-200 Częstochowa		
BRANŻA	ARCHITEKTURA KRAJOBRAZU		
TRZES RYSUNKU	WYMIARY		
PROJEKTOWAŁ	mgr inż. arch. kraj. Ewelina Turek		
ZESPÓŁ PROJEKTOWY	mgr inż. arch. kraj. Ewelina Turek		
STADIUM	SKALA	DATA	NR RYSUNKU
projekt wykonawczy	1:150	03.2025	A2